




M1

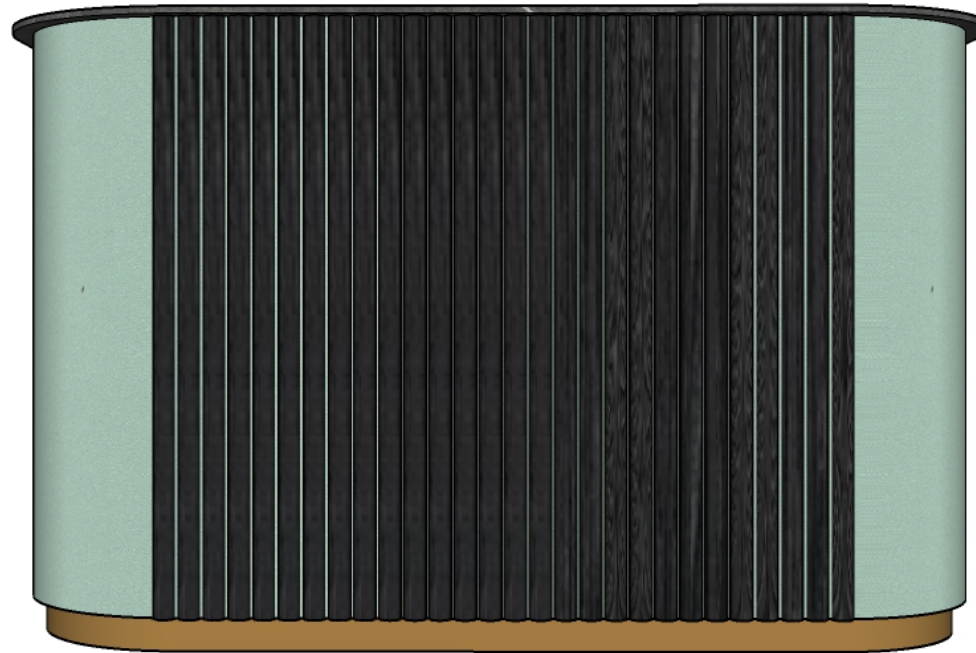

M1

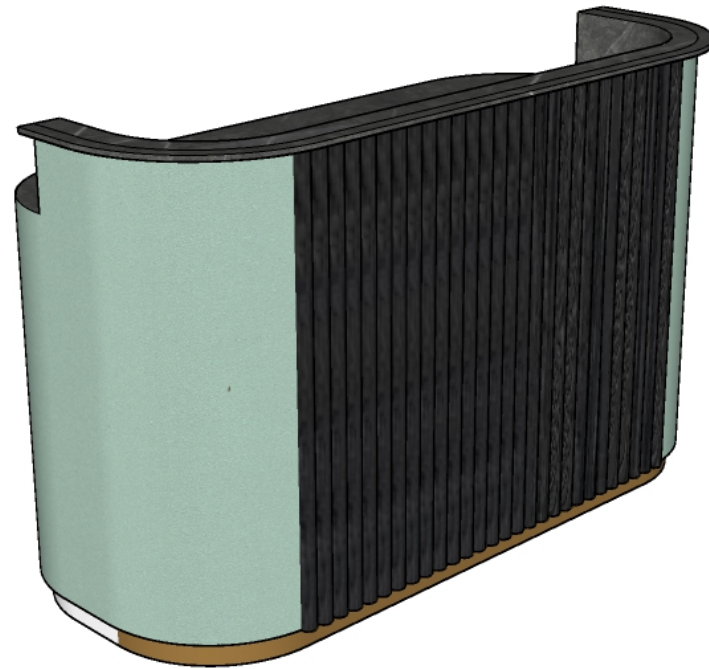


M2

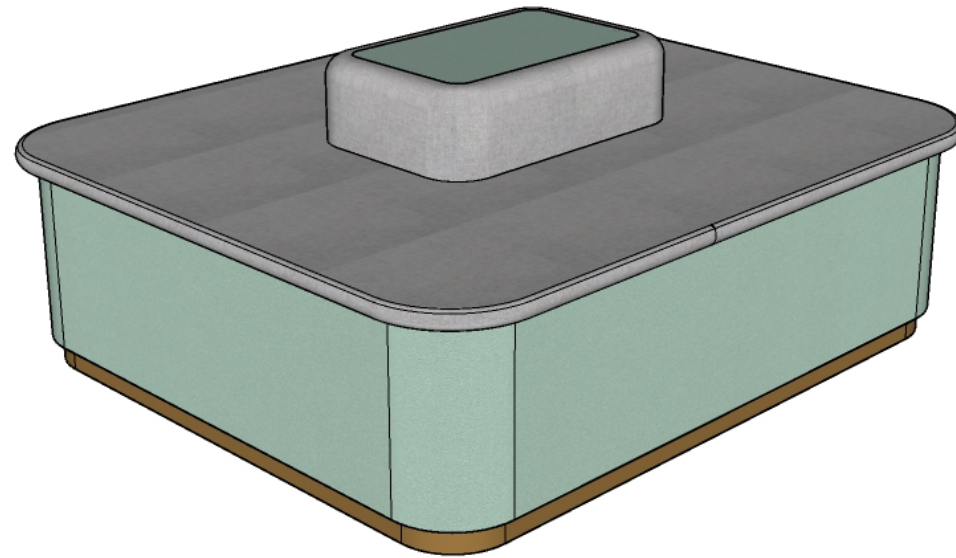

M3



M4

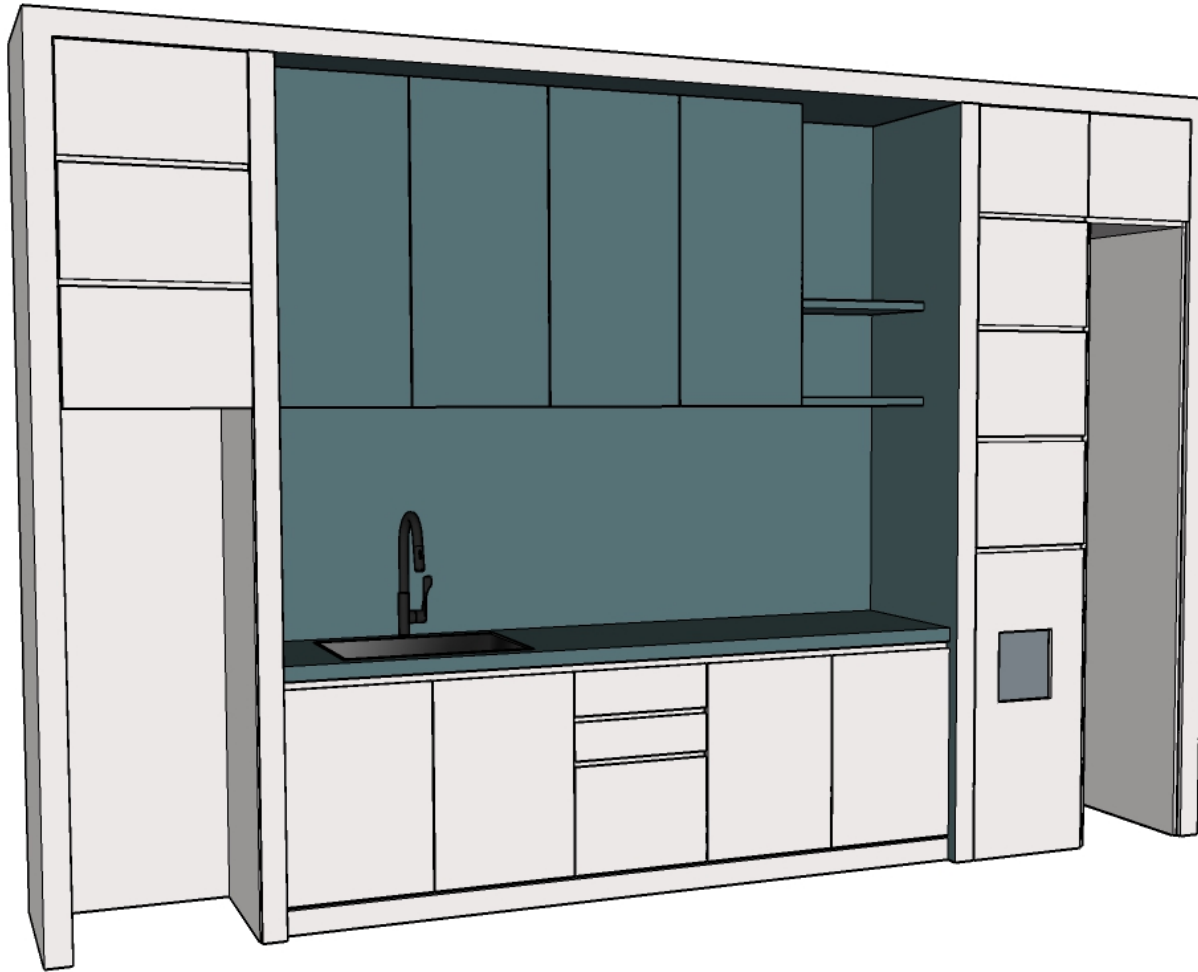

M5

KEZTA
PVC INTER

WOOD SERIES...

SOLID SERIES...

MARBLE SERIES...

LEATHER SERIES...


STEEL SERIES...

CONCRETE SERIES...

LINEN SERIES...

ARKILENS



M6

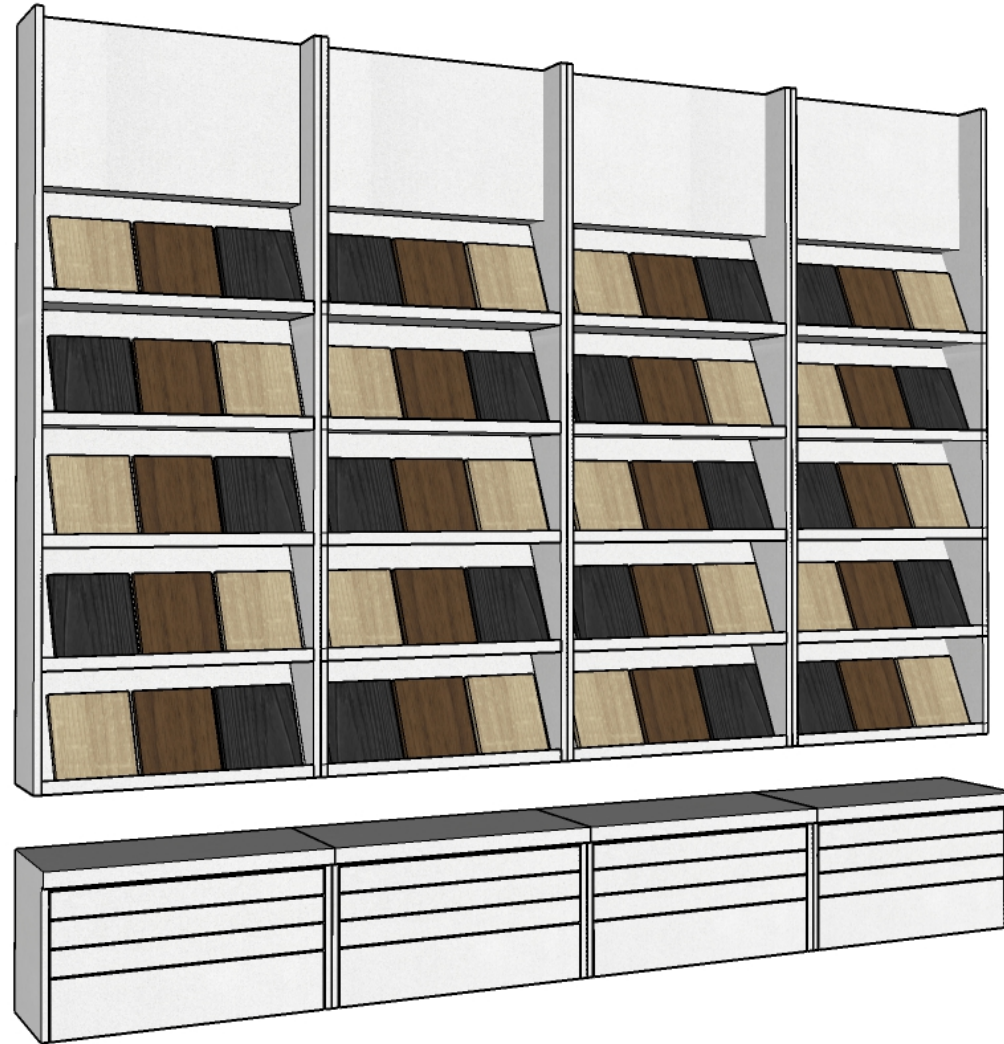



M7




M8

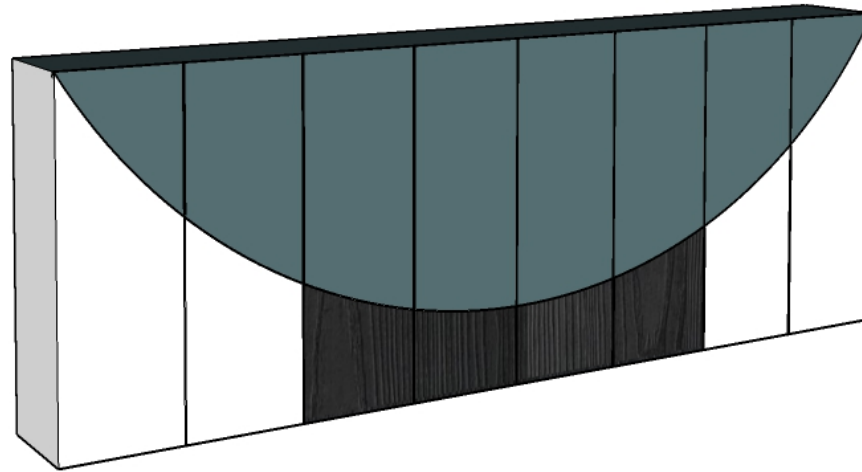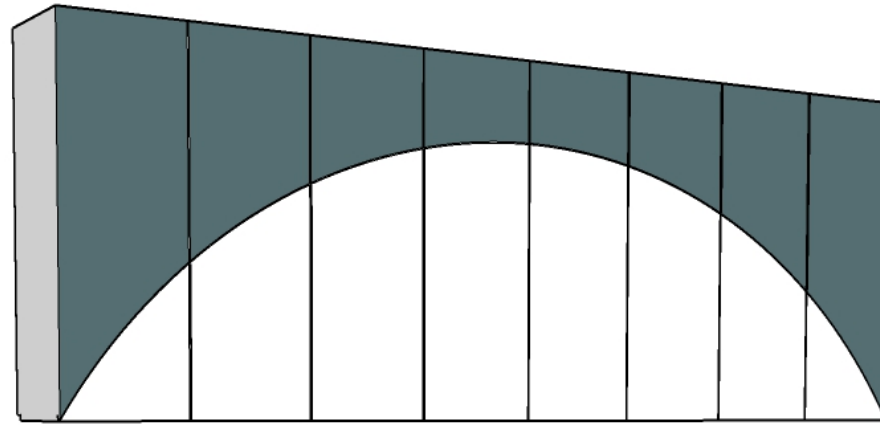


M9

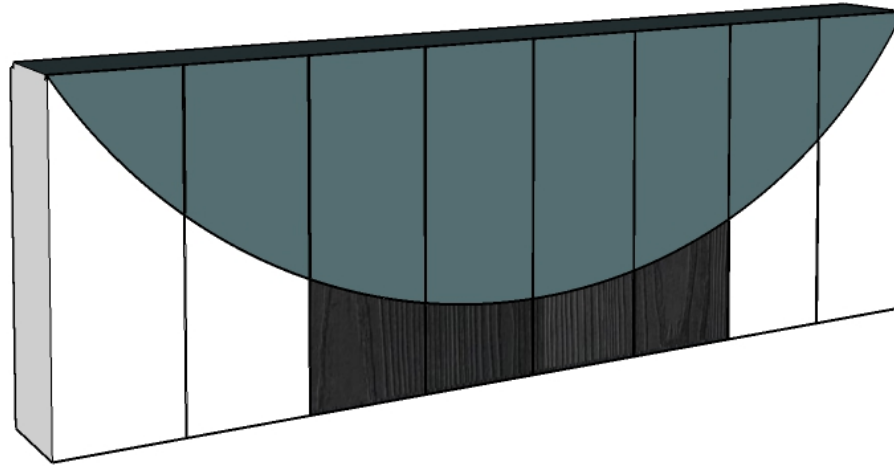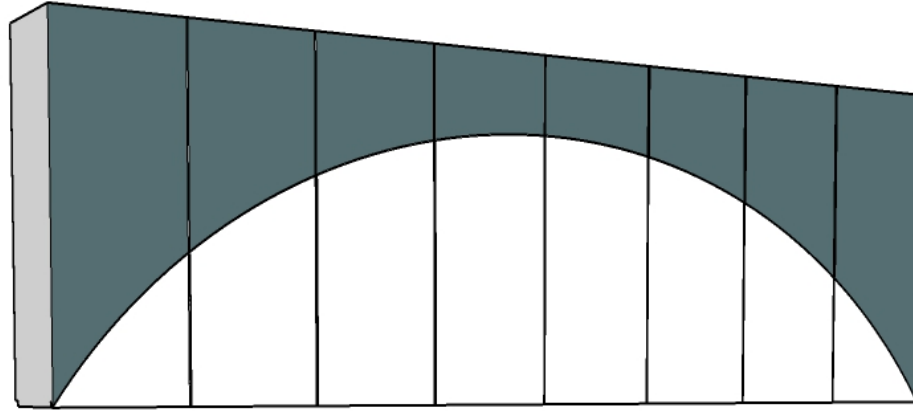

M10

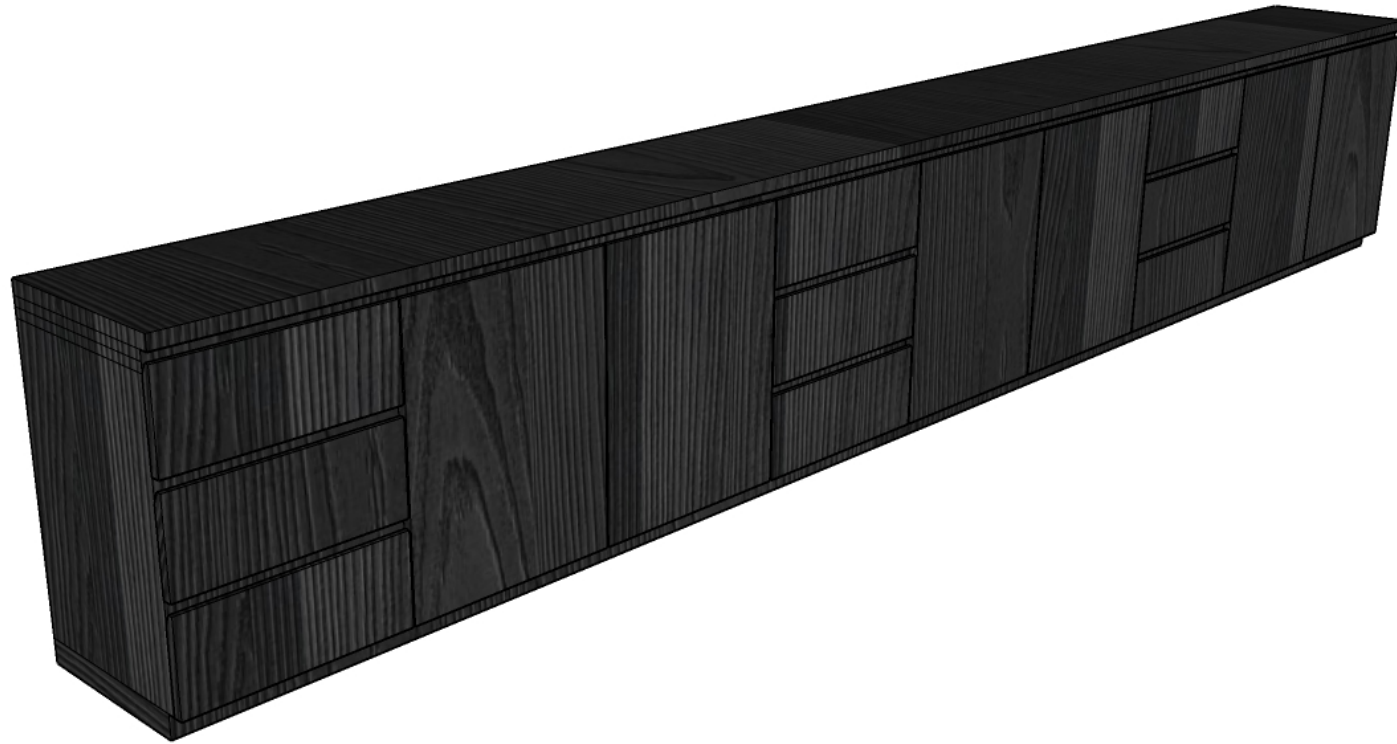

M11

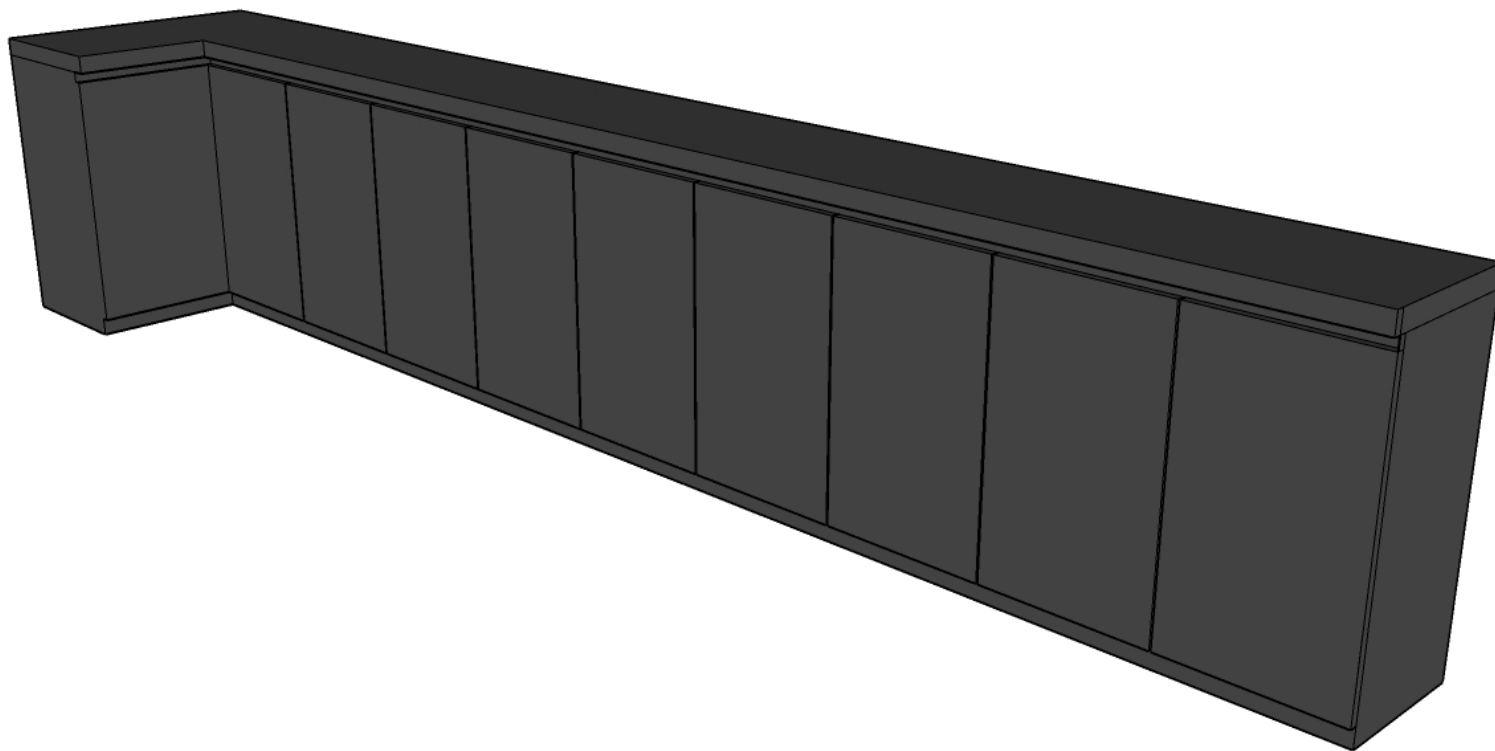



M13



M12




M14

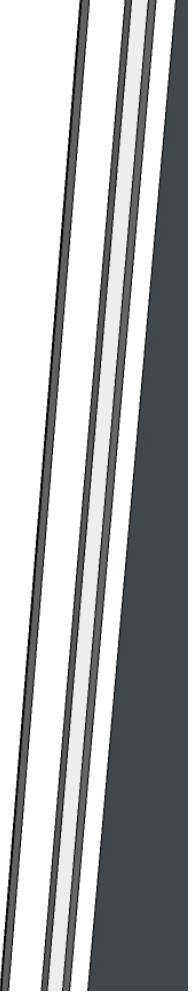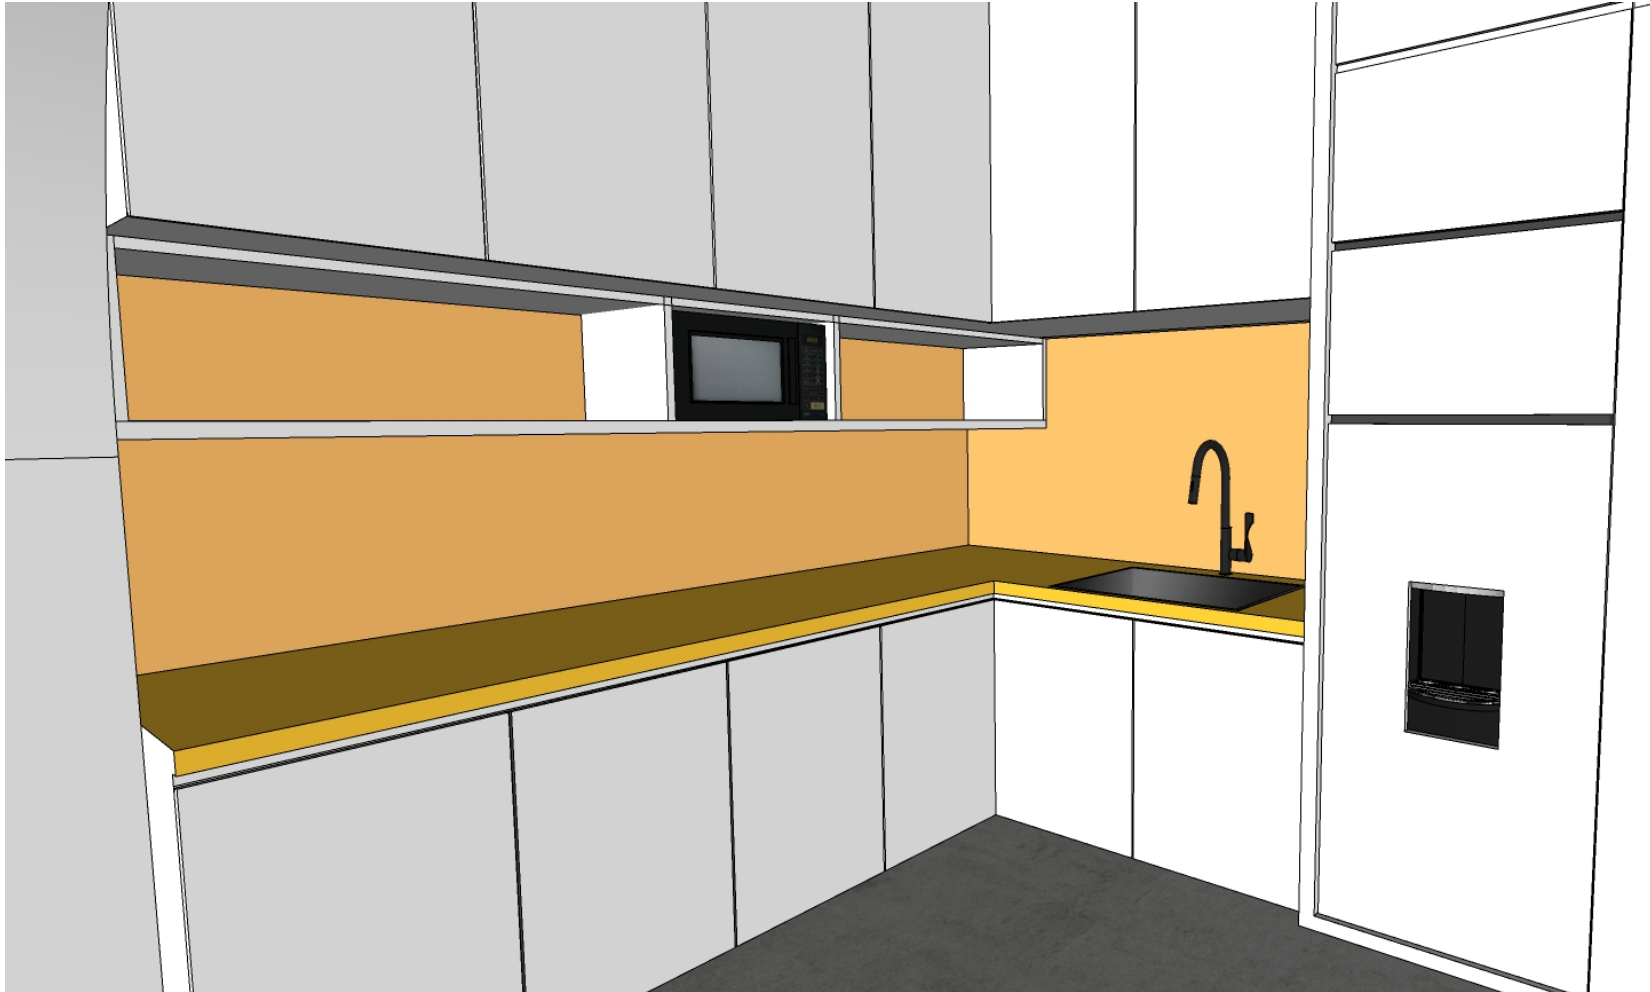


M15




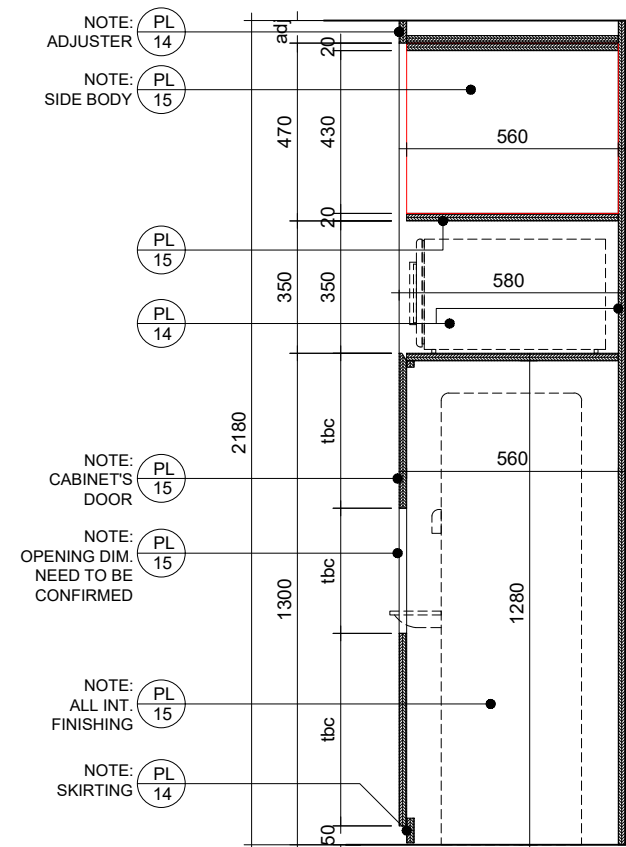

4
-
PANTRY-SECT
SCALE 1 : 20

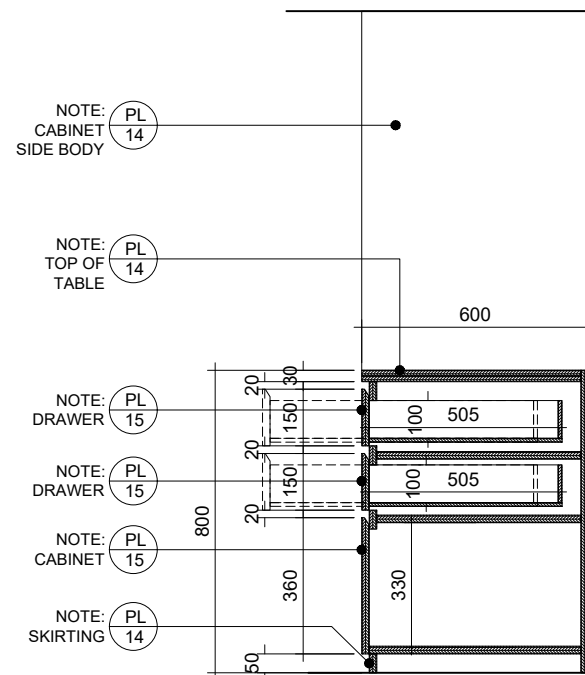

3
-
PANTRY-SECT
SCALE 1 : 20

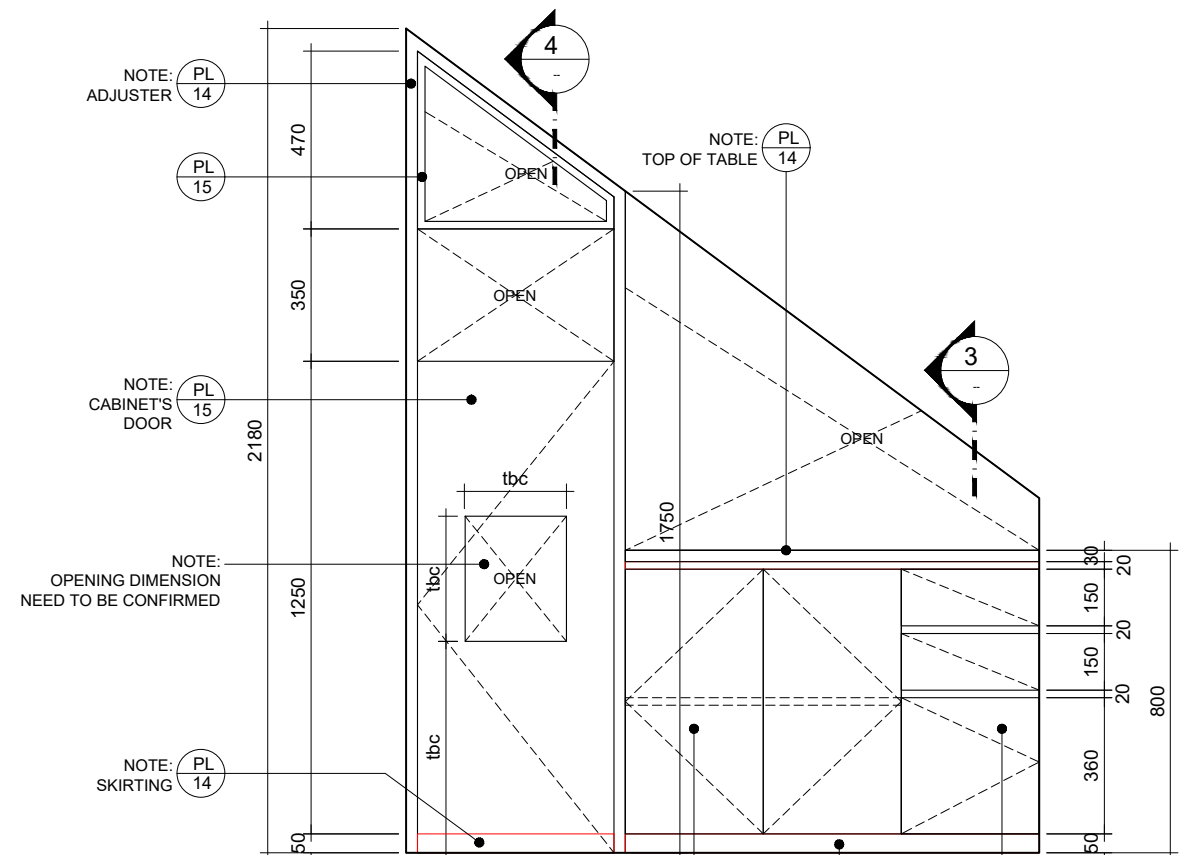


2
-
PANTRY DETAIL - ELEV
SCALE 1 : 20



M16

3D IMAGE AS REFERENCE ONLY,
ALL DIMENSION MUST SEE AT
DETAIL DRAWING

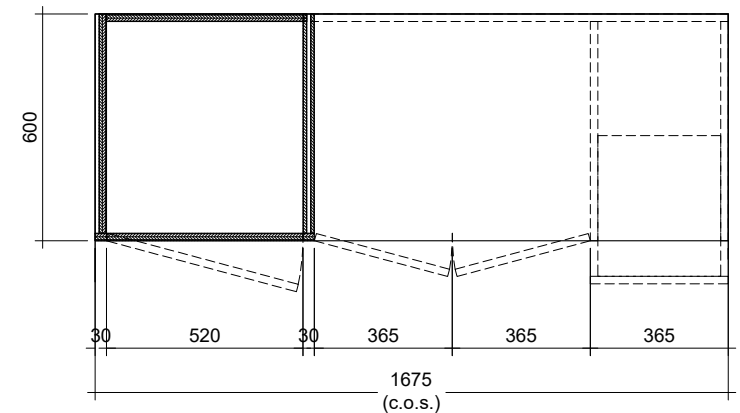

1
-
PANTRY DETAIL - PLAN
SCALE 1 : 20

INTERIOR CONSULTANT :



DUTA HARAPAN INDAH
NO 19 UU
KAPUK MUJARA, PENJARINGAN
JAKARTA UTARA, 14460
Ph. (021) 8626805

www.arkilens.com

PROJECT :

STA GROUP OFFICE
TANGERANG
INDONESIA

DRAWING NAME :

M16 - CABINET TY.3
DETAIL

DRAWN BY

WL

CHECKED

AW

APPROVED :

SHEET NO

A15-16

SCALE

1 : 10

DATE

19-07-2021

NO.

NOTES & REVISION

- 01 DETAIL DRAWING A10 01-04 & NEW MAT
- 02 NEW OPENING 2ND FLOOR
- 03 PANTRY CABINET DETAIL REV


WRITTEN DIMENSION OF THESE DRAWINGS SHALL HAVE
TO BE VERIFIED BY CONTRACTOR BEFORE STARTING THE
PROJECT. THE CONTRACTOR SHALL BE RESPONSIBLE FOR
DIMENSIONS AND CONDITIONS ON SITE.

UKURAN YANG TERtera DALAM GAMBAR - GAMBAR INI
HARUS DIPERIKSA ULANG OLEH KONTRAKTOR SEBELUM
MELAKSANAKAN PROYEK. KONTRAKTOR HARUS
BERTANGGUNG JAWAB ATAS SEMUA UKURAN DAN
KEADAAN DIPROYEK.

M17




M18

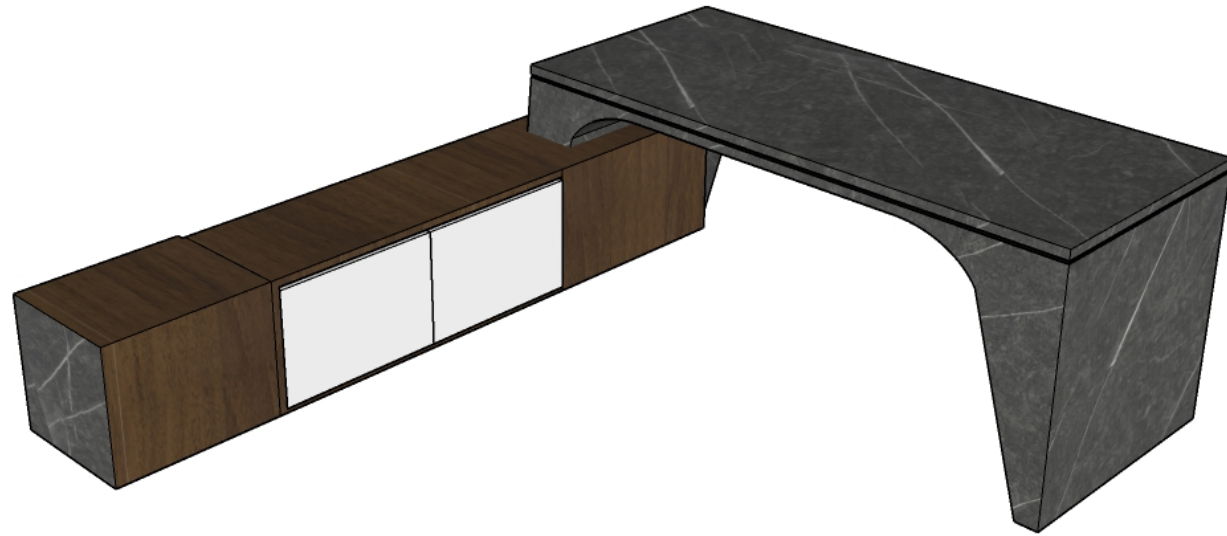

M18




M19

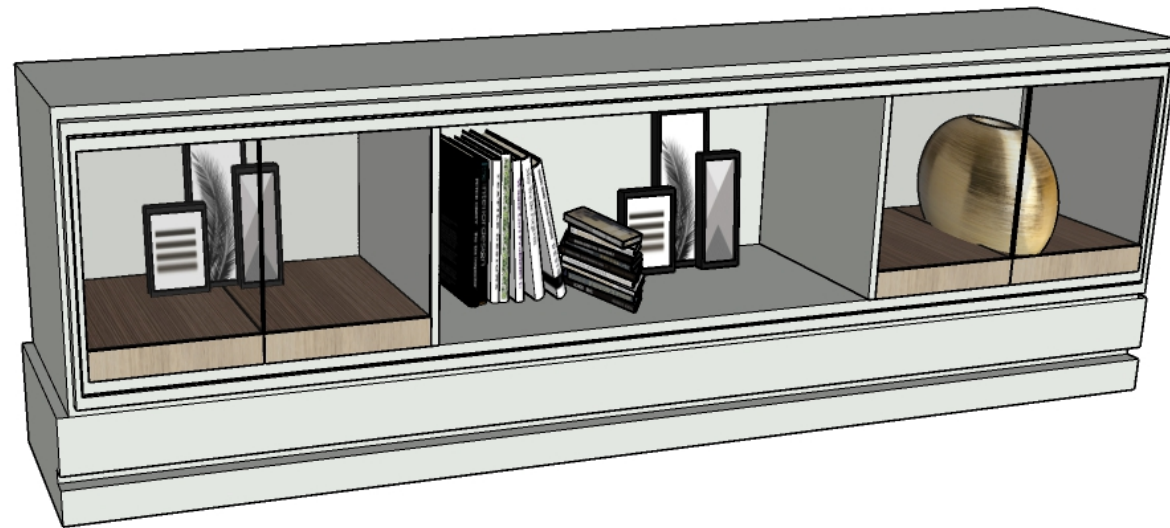

M20



M21

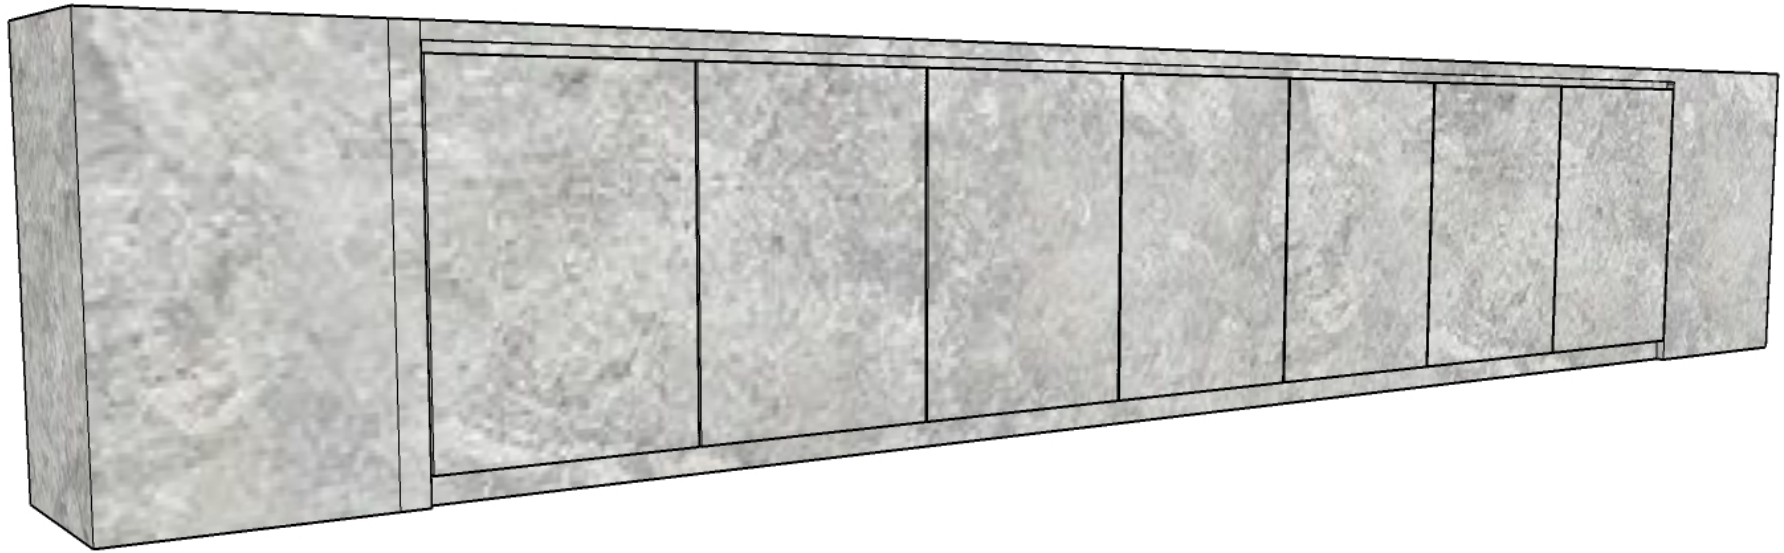

M22A-B



M23AB

